
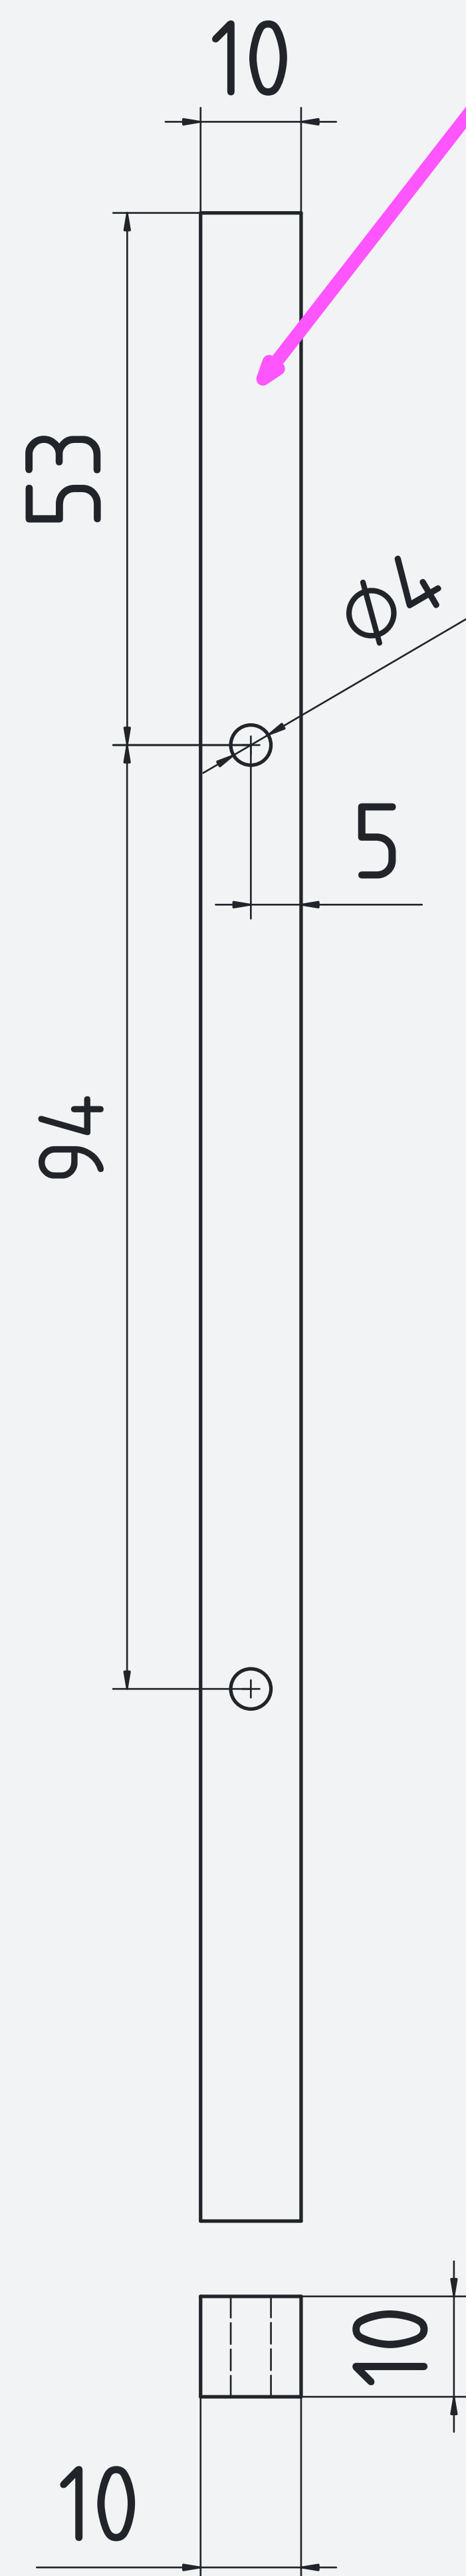
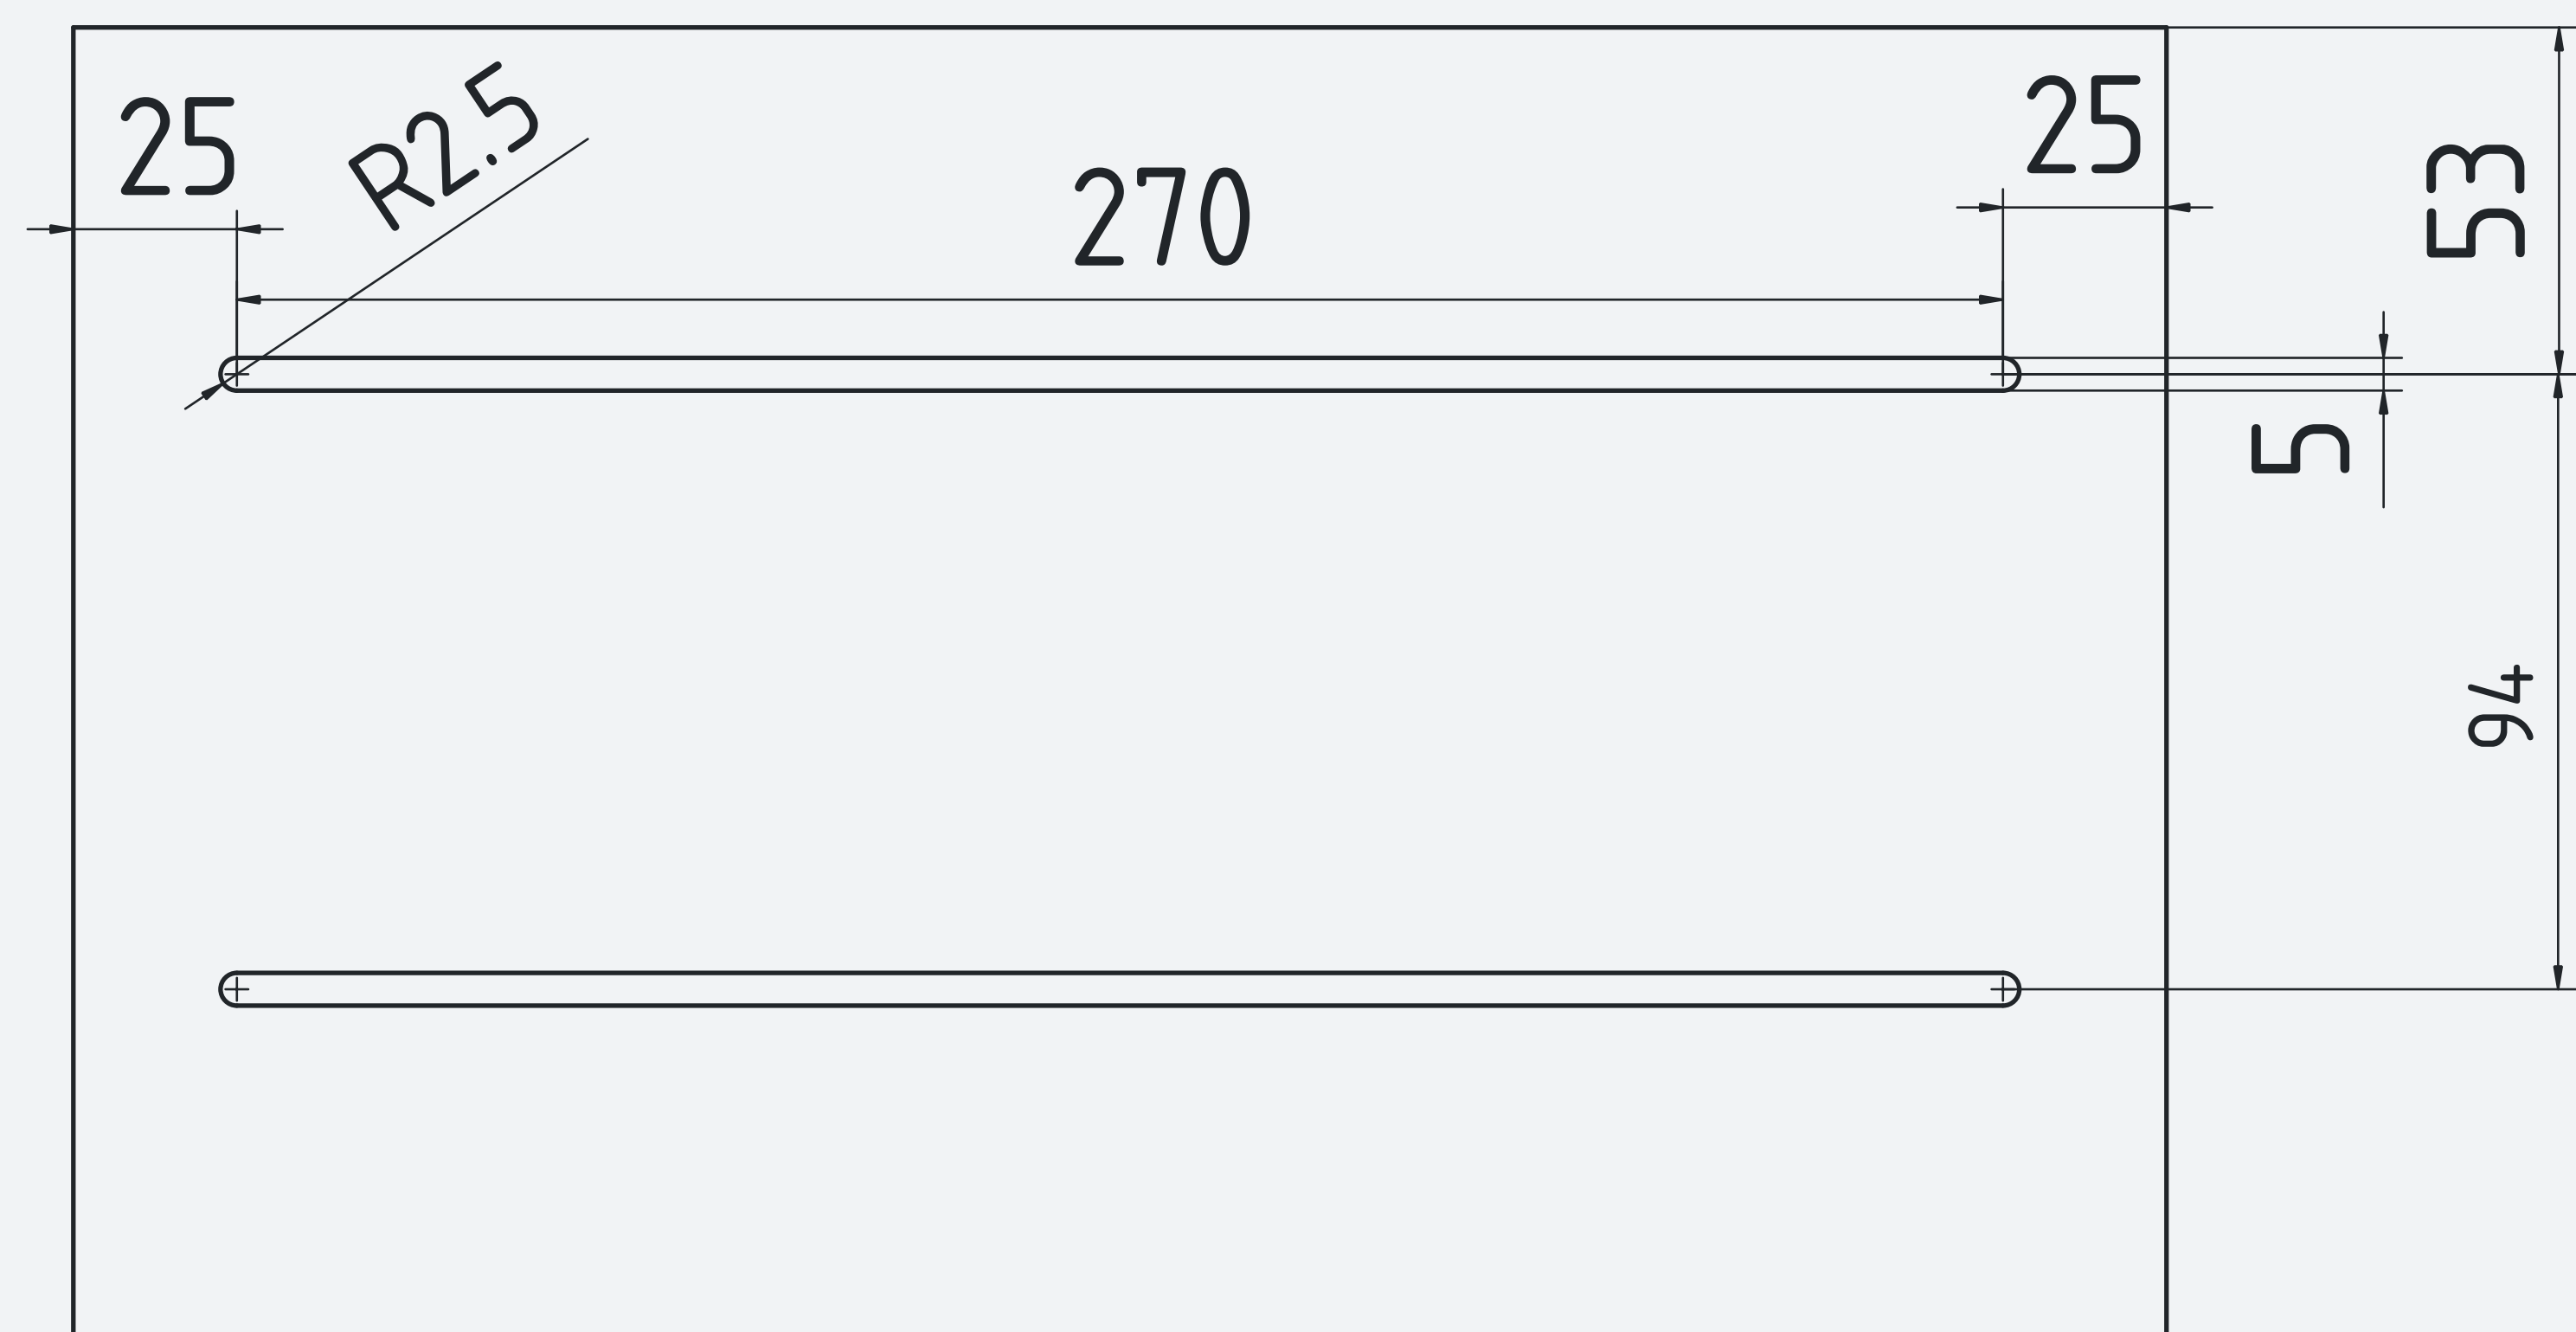
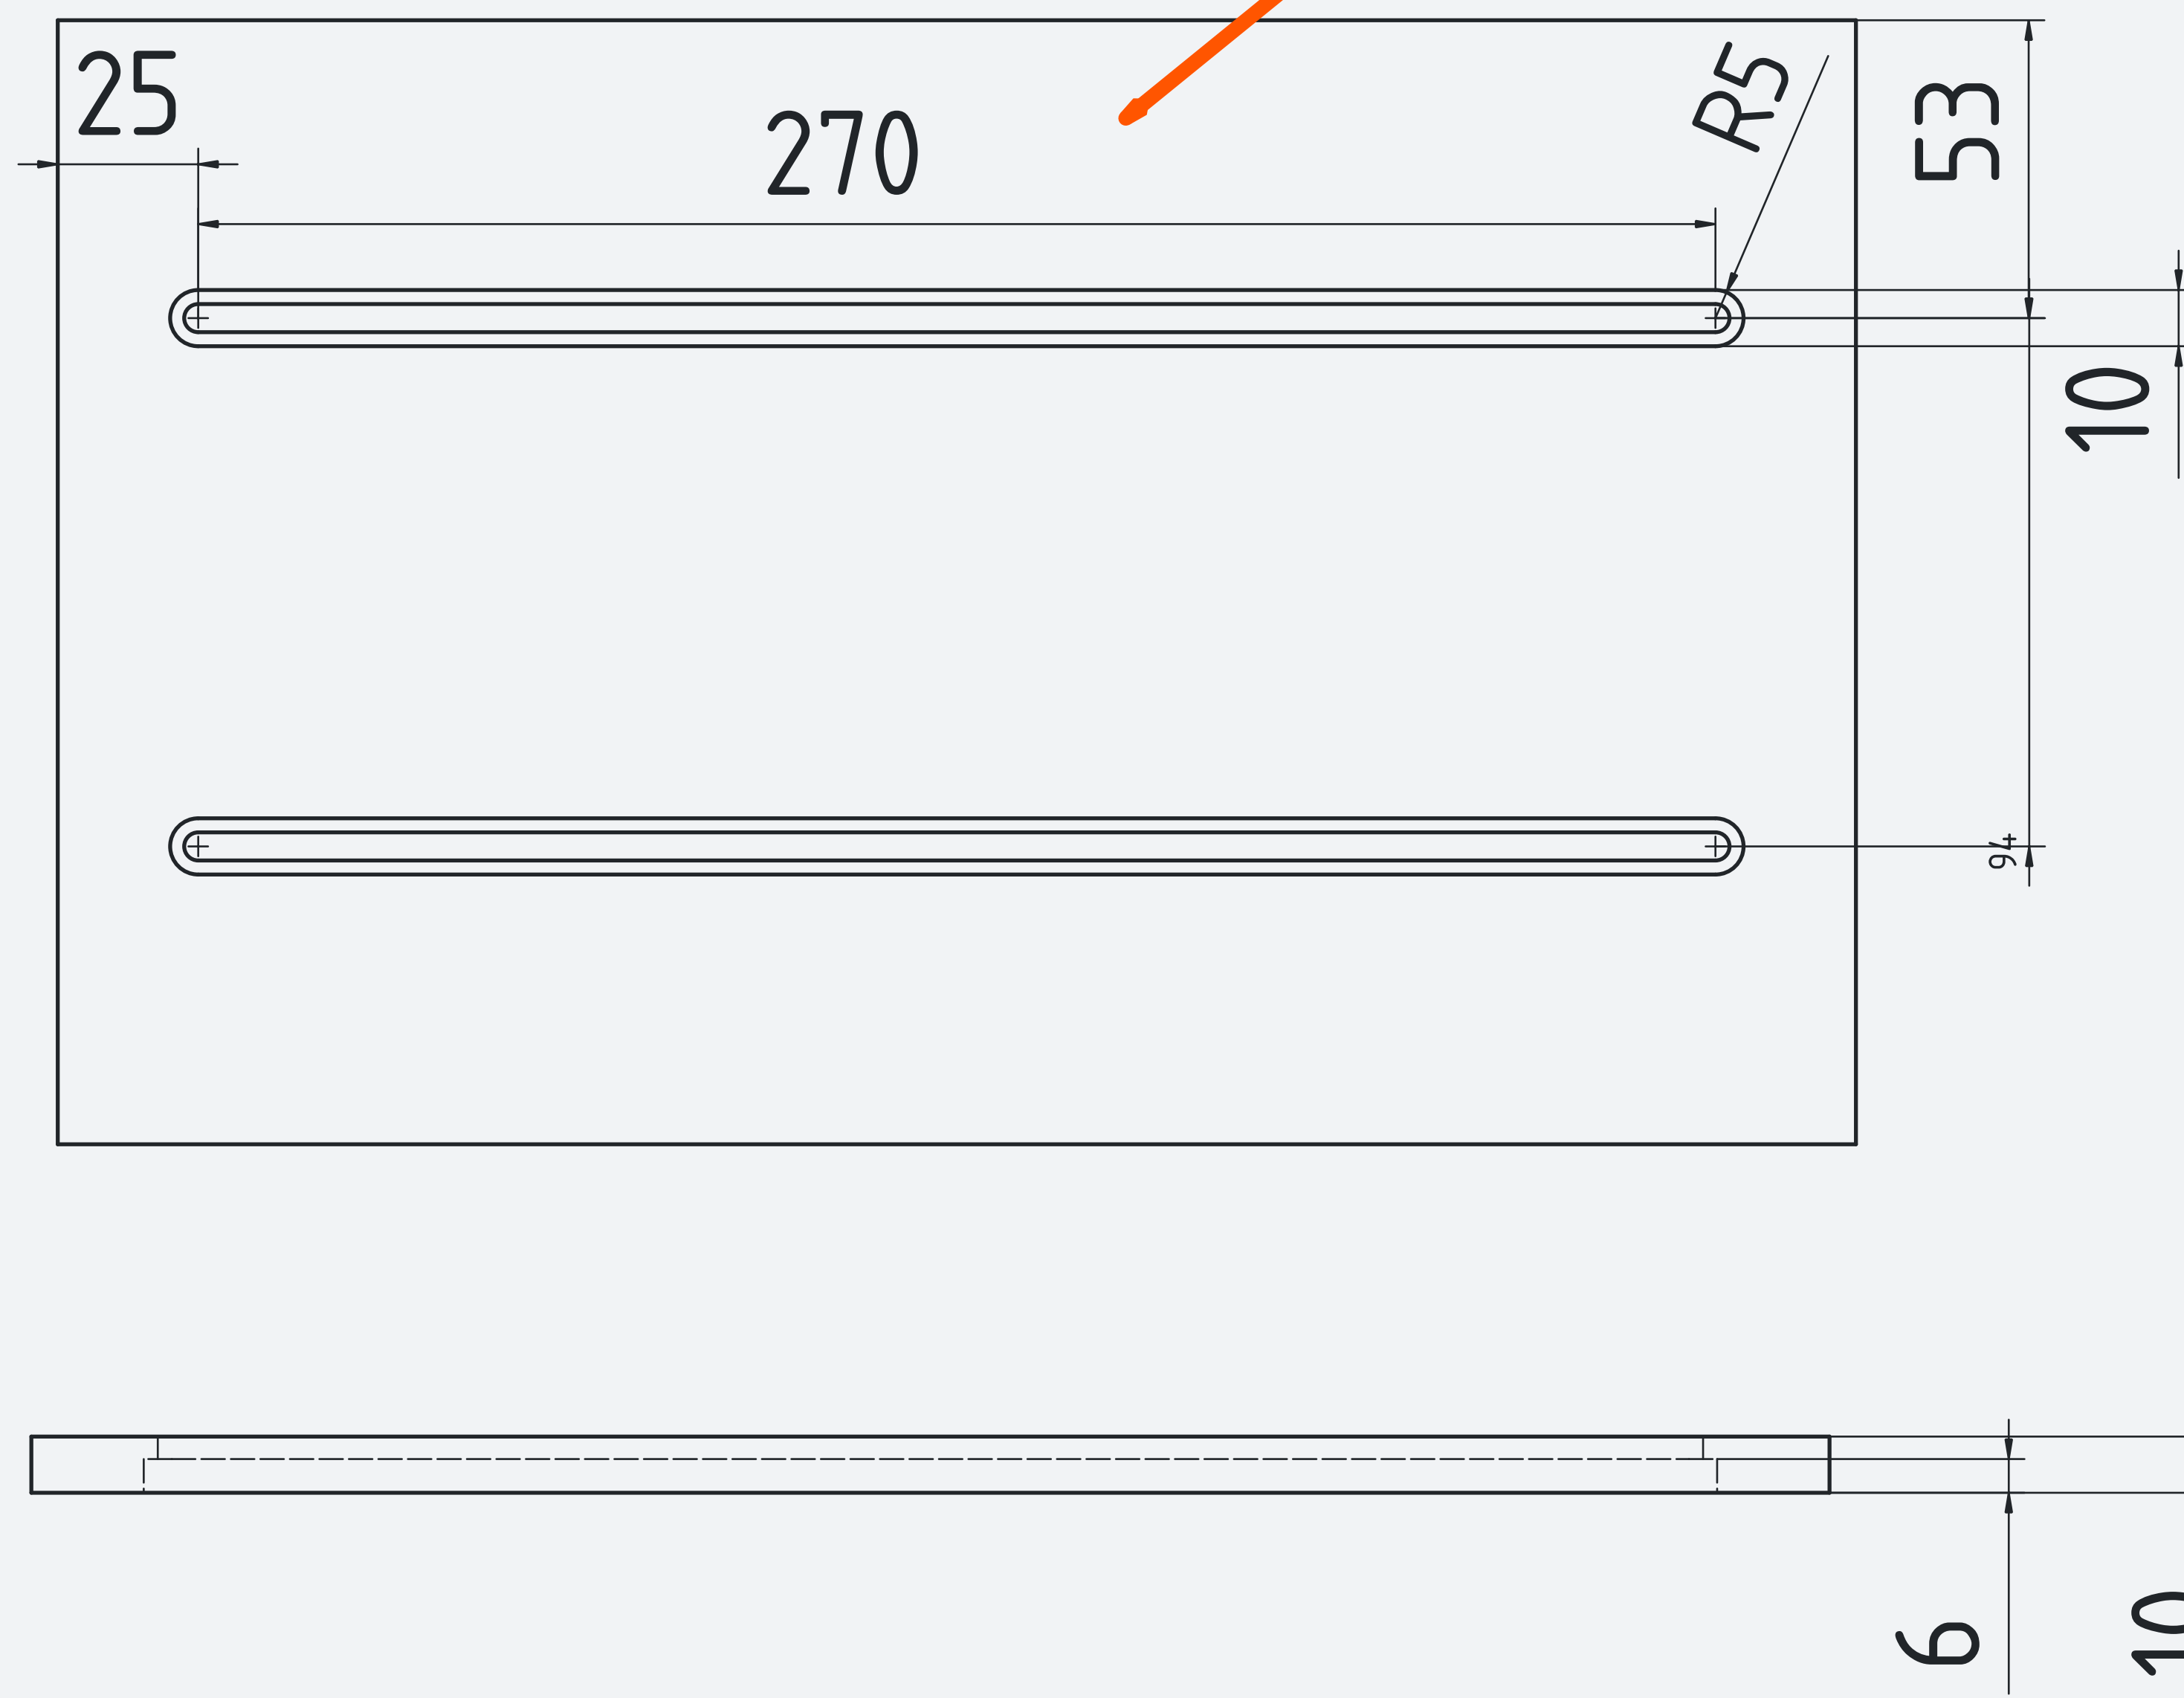
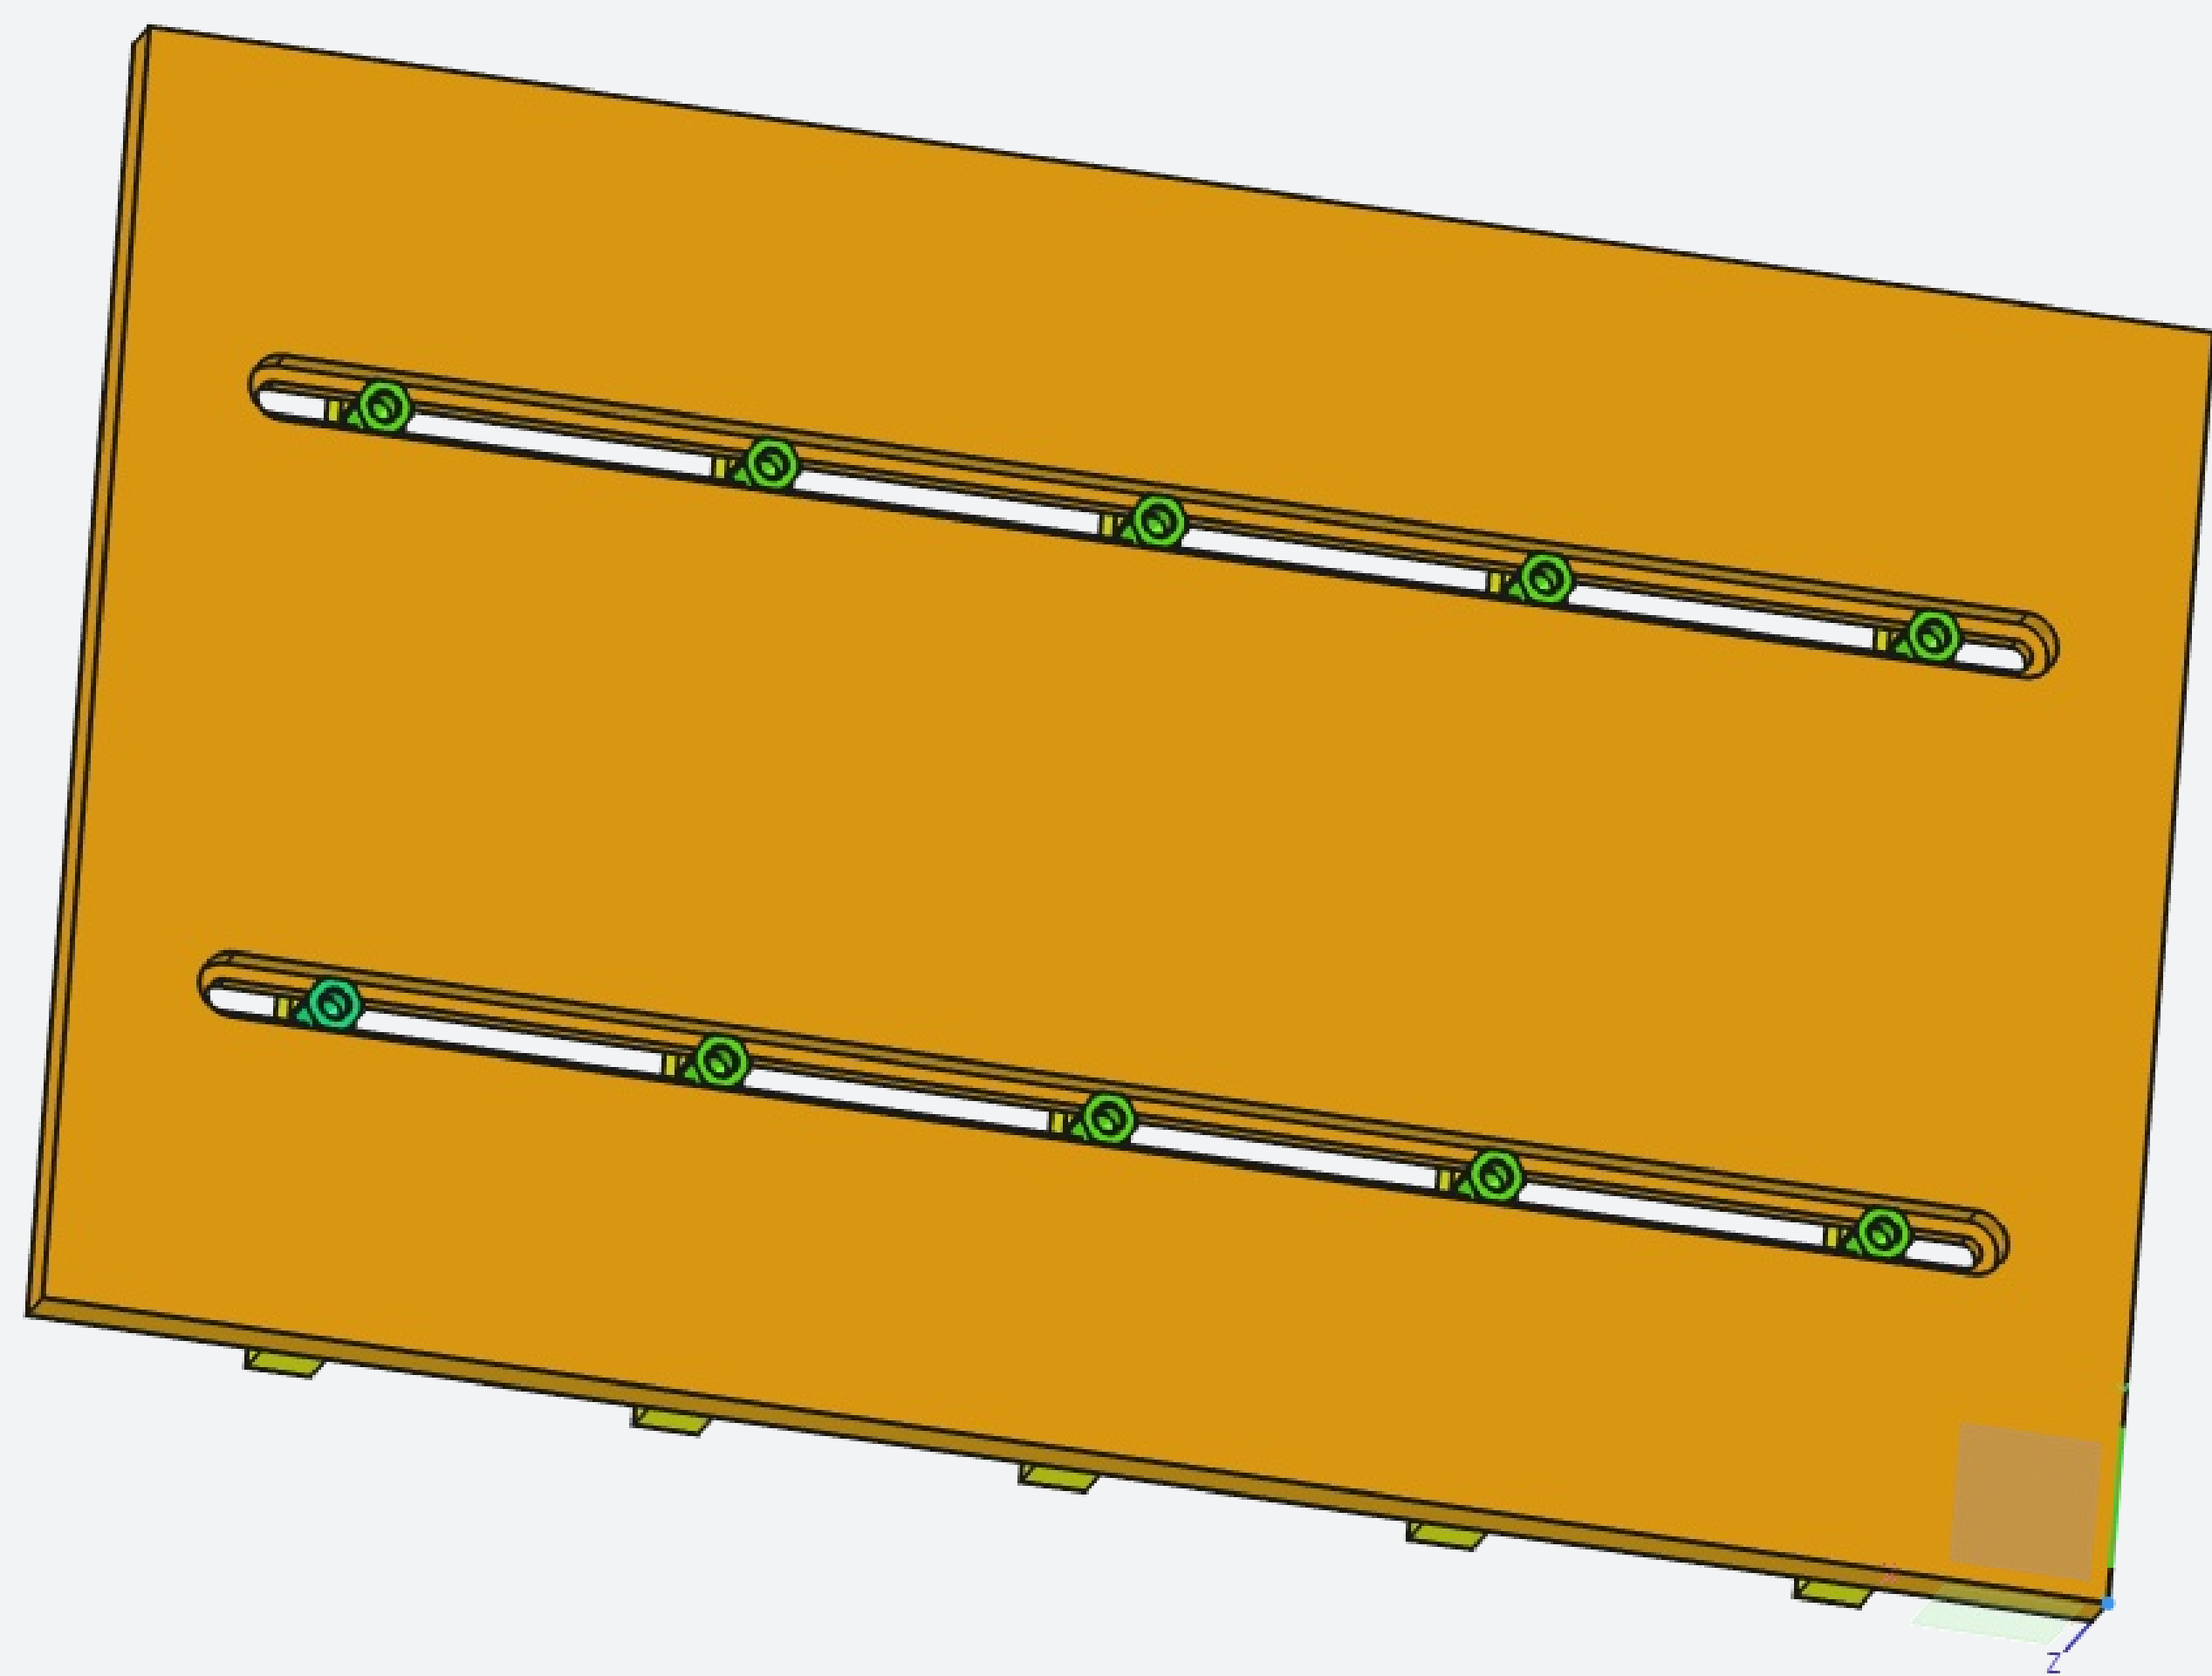
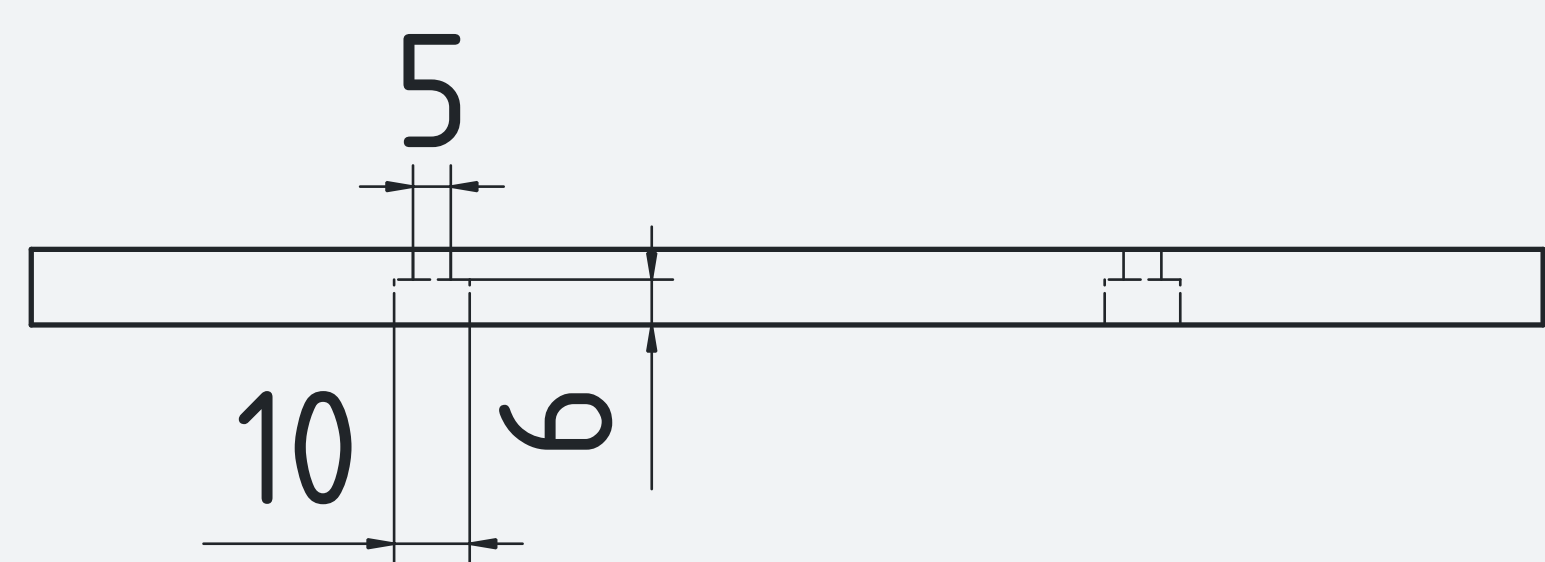


Part 1: Để có cắt rãnh x5 pcs

Part 2: Các thanh ngang khoảng cách x25 pcs

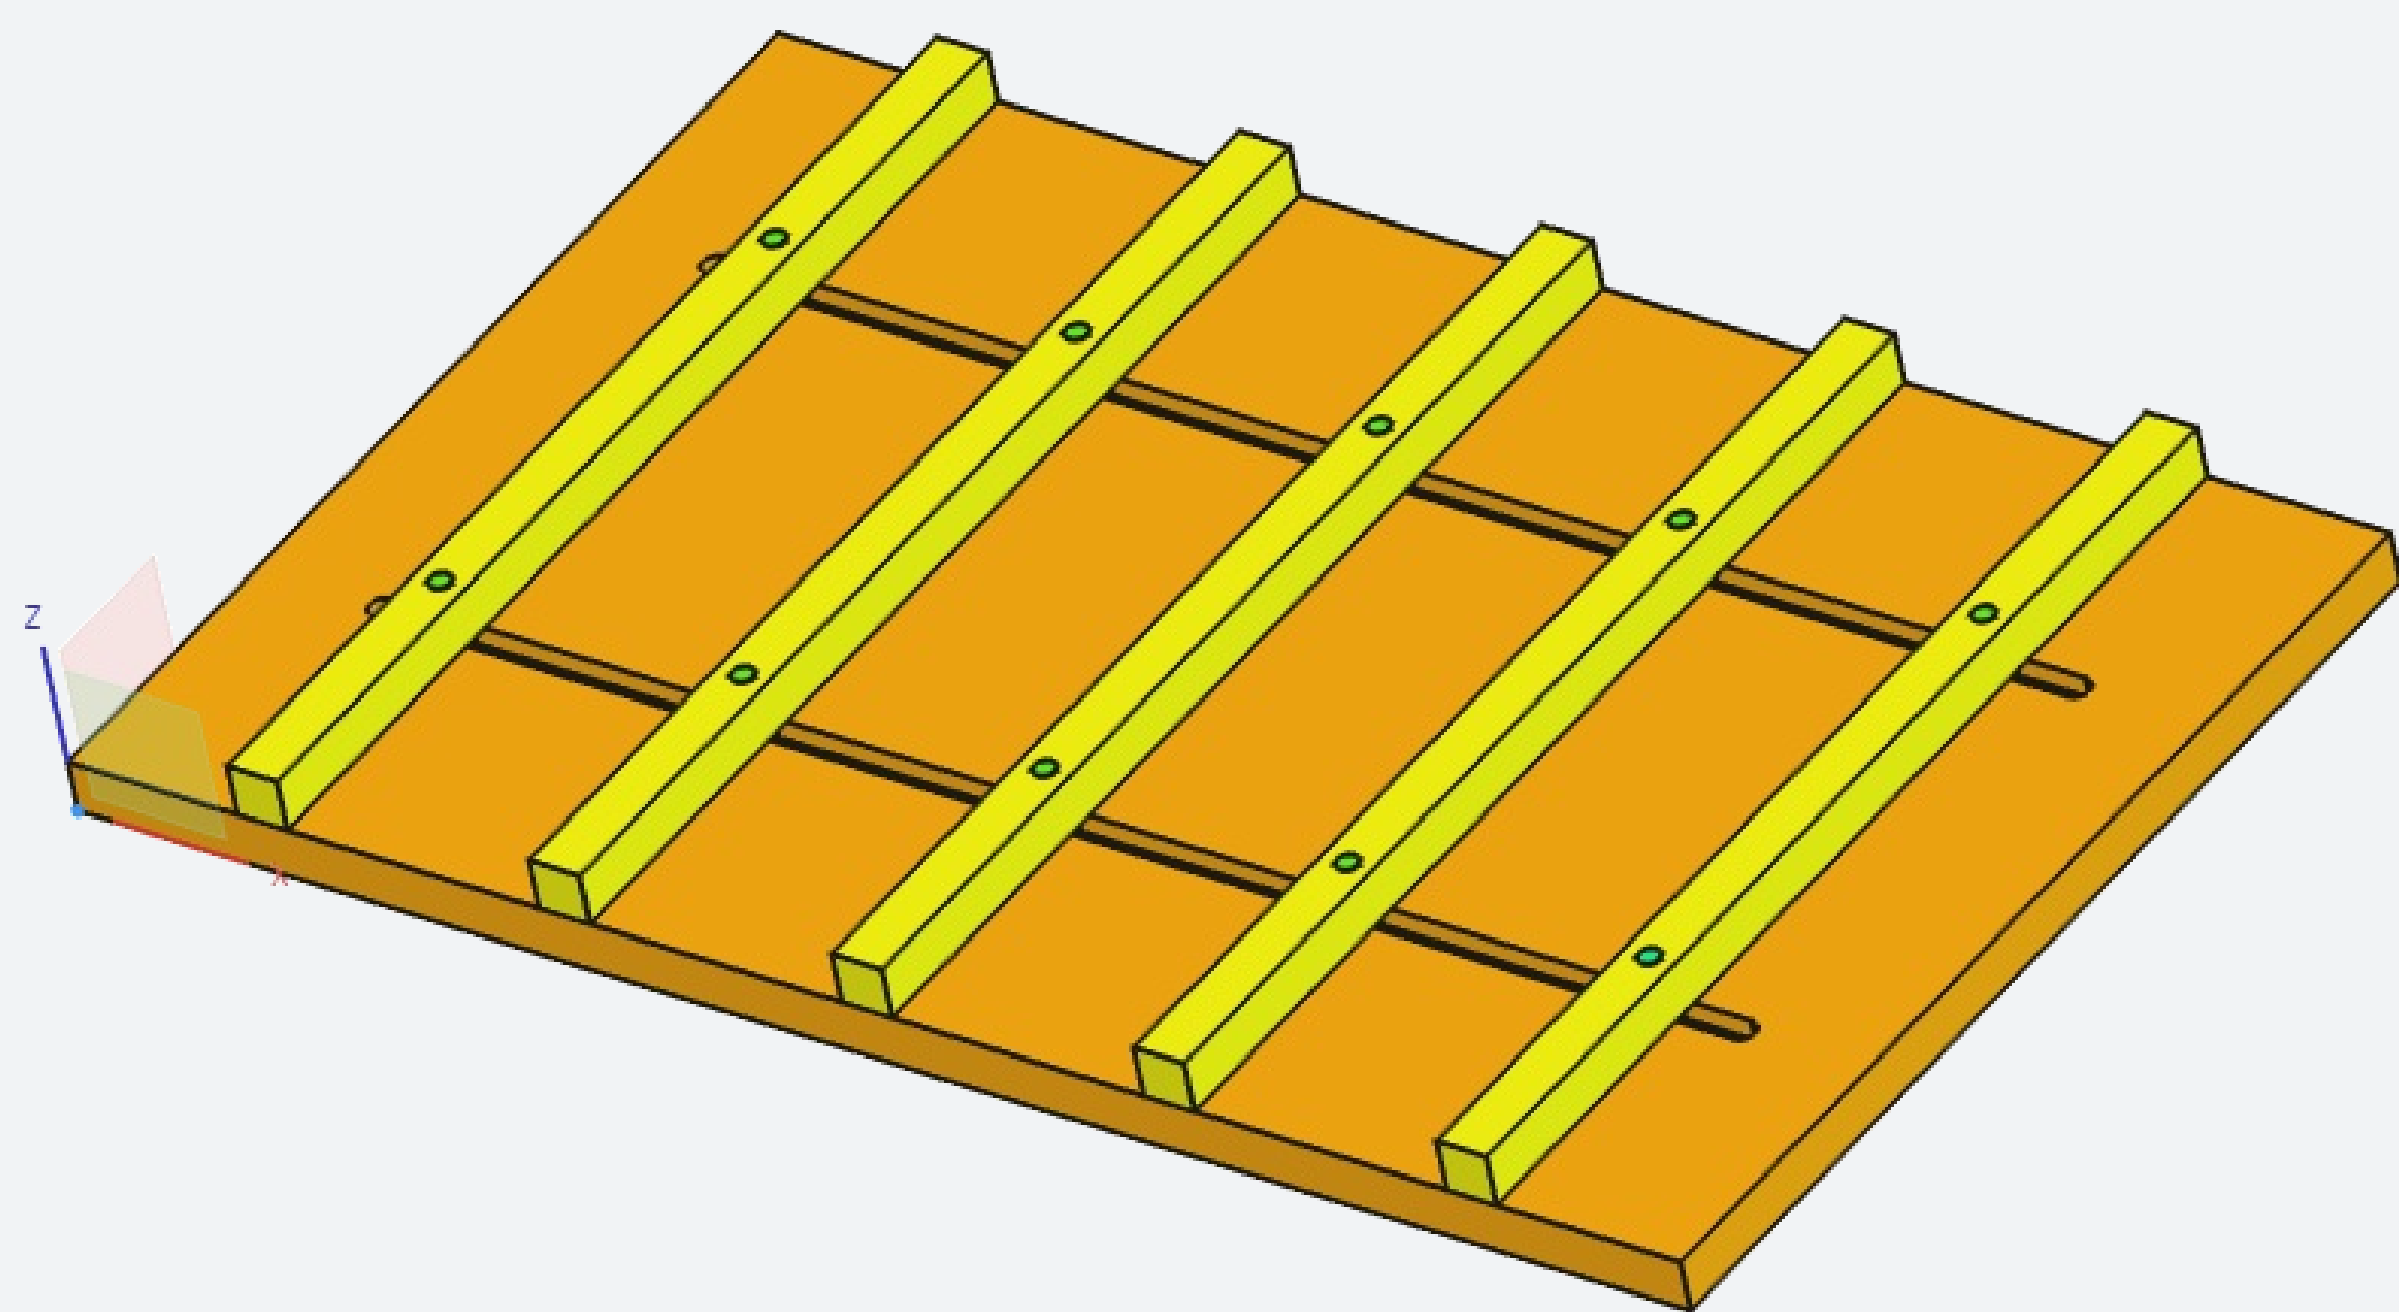

TÊN	NGÀY	SL Part1)	SL (Part2)	VẬT LIỆU
TÂM	05/08/2026	5	25	PHÍP